

PROJEKT DOMU KULTURY PRZY ULICY SZUBIŃSKIEJ POZNAŃ

BUDYNEK ZOSTAŁ ZAPROJEKTOWANY Z PRZEZNACZENIEM NA PROPAGOWANIE KULTURY I SZTUKI WŚRÓD MIESZKAŃCÓW ŚWIERCZEWIA W POZNANIU ORAZ INTEGRACJĘ LOKALNEJ SPOŁECZOŚCI. FORMA BUDYNKU JEST PROSTA, ZŁOŻONA Z DWÓCH BRYŁ, KTÓRE ZOSTAŁY PRZESUNIĘTE WZGLĘDEM SIEBIE, TAK ABY PRZEDŁUŻYĆ OŚ WIDOKOWĄ ORAZ SKIEROWAĆ WZROK OBSERWATORA KU WAŻNEJ DOMINANCIE W OKOLICY - FORT IX.


LOKALIZACJA



LEGENDA


- OBSZAR OPRACOWYWYWA
- MAX NIEPRZEKRACZALNA LINIA ZABUDOWY
- ZABUDOWA MIESZKANIOWA
- ZIELEŃ WYSOKA
- DOMINANTA
- DROGA LOKALNA
- DROGA DOJAZDOWA
- OŚ WIDOKOWA

RZUT PARTERU SKALA 1:100

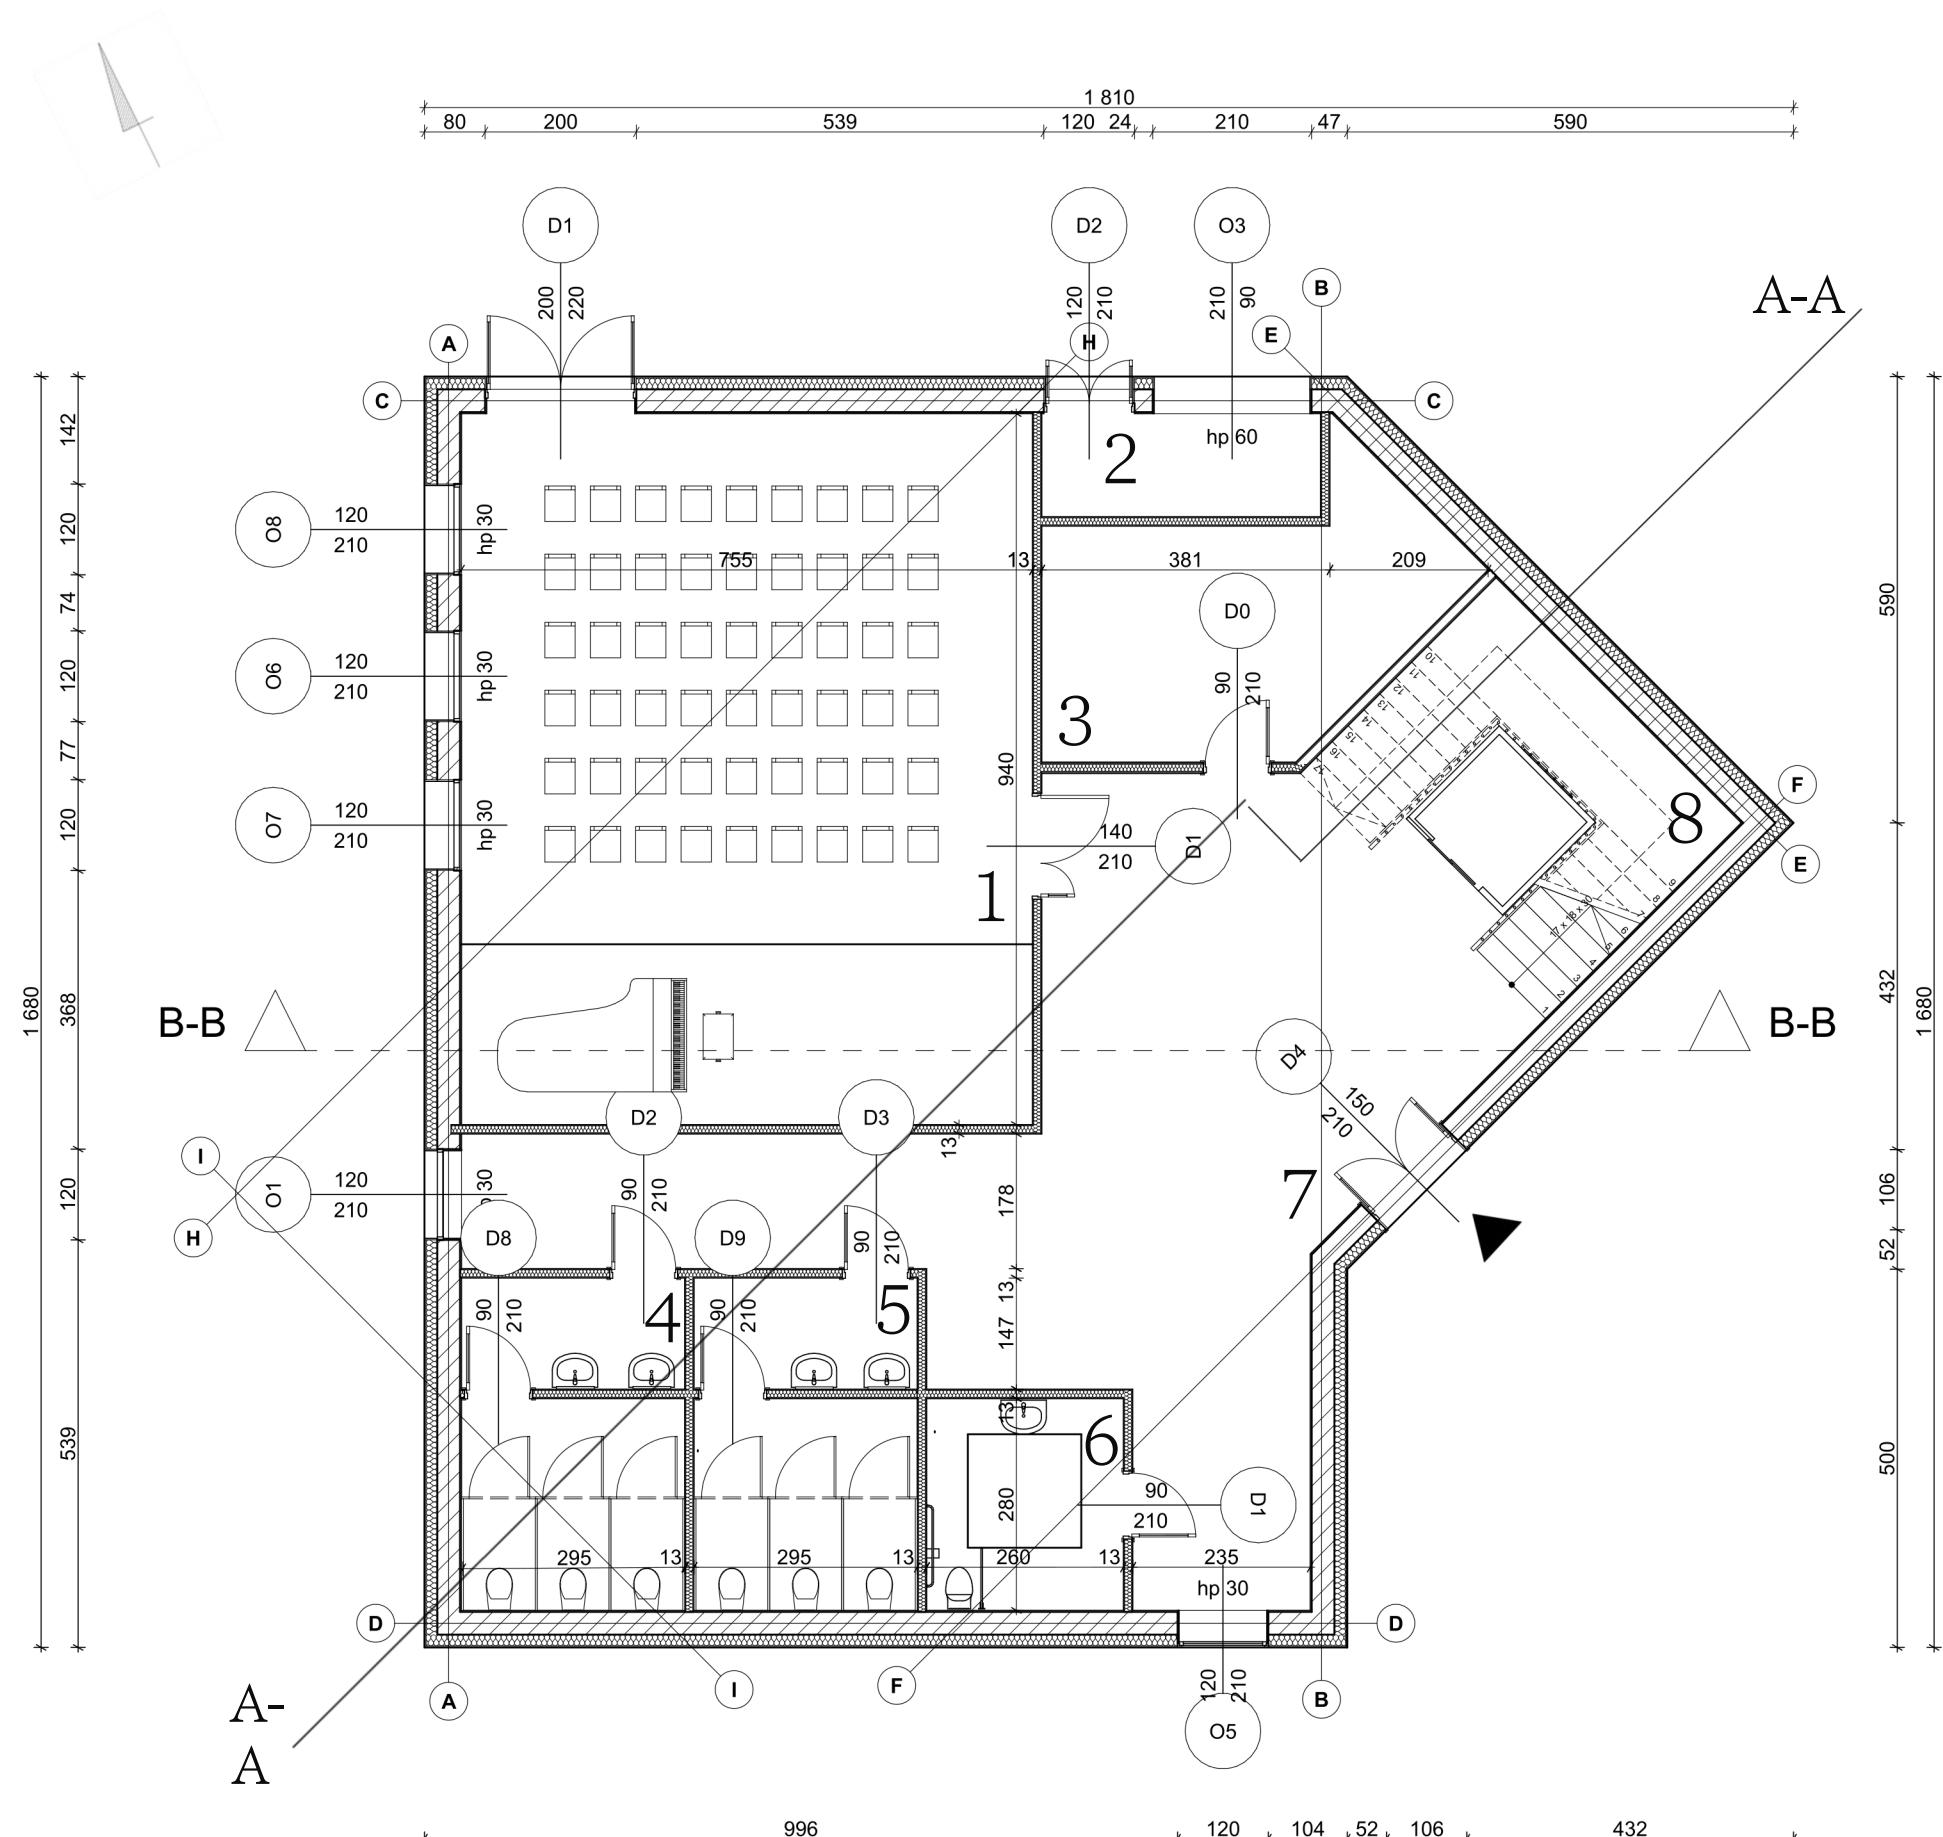


| nr | Powierzchnia m ² | Rodzaj pomieszczenia |
|-----------------------------|-----------------------------|-------------------------------|
| 1 | 70,93 | Sala koncertowa |
| 2 | 5,02 | Pomieszczenie na odpady |
| 3 | 16,12 | Pomieszczenie techniczne |
| 4 | 12,96 | WC damskie |
| 5 | 12,96 | WC męskie |
| 6 | 7,25 | WC dla niepełnosprawnych |
| 7 | 61,52 | Hol + korytarz |
| 8 | 16,91 | Klatka schodowa |
| 9 | 46,64 | Hol |
| 10 | 24,80 | Sklepik |
| 11 | 5,08 | Pomieszczenie socjalne |
| 12 | 30,04 | Sala na zespół |
| 13 | 12,52 | Pomieszczenie dla pracowników |
| 14 | 14,40 | Administracja |
| 15 | 26,87 | Sala chóralna |
| RAZEM POWIERZCHNI UŻYTKOWEJ | | 364,02 m ² |


WNIOSKI Z ANALIZ

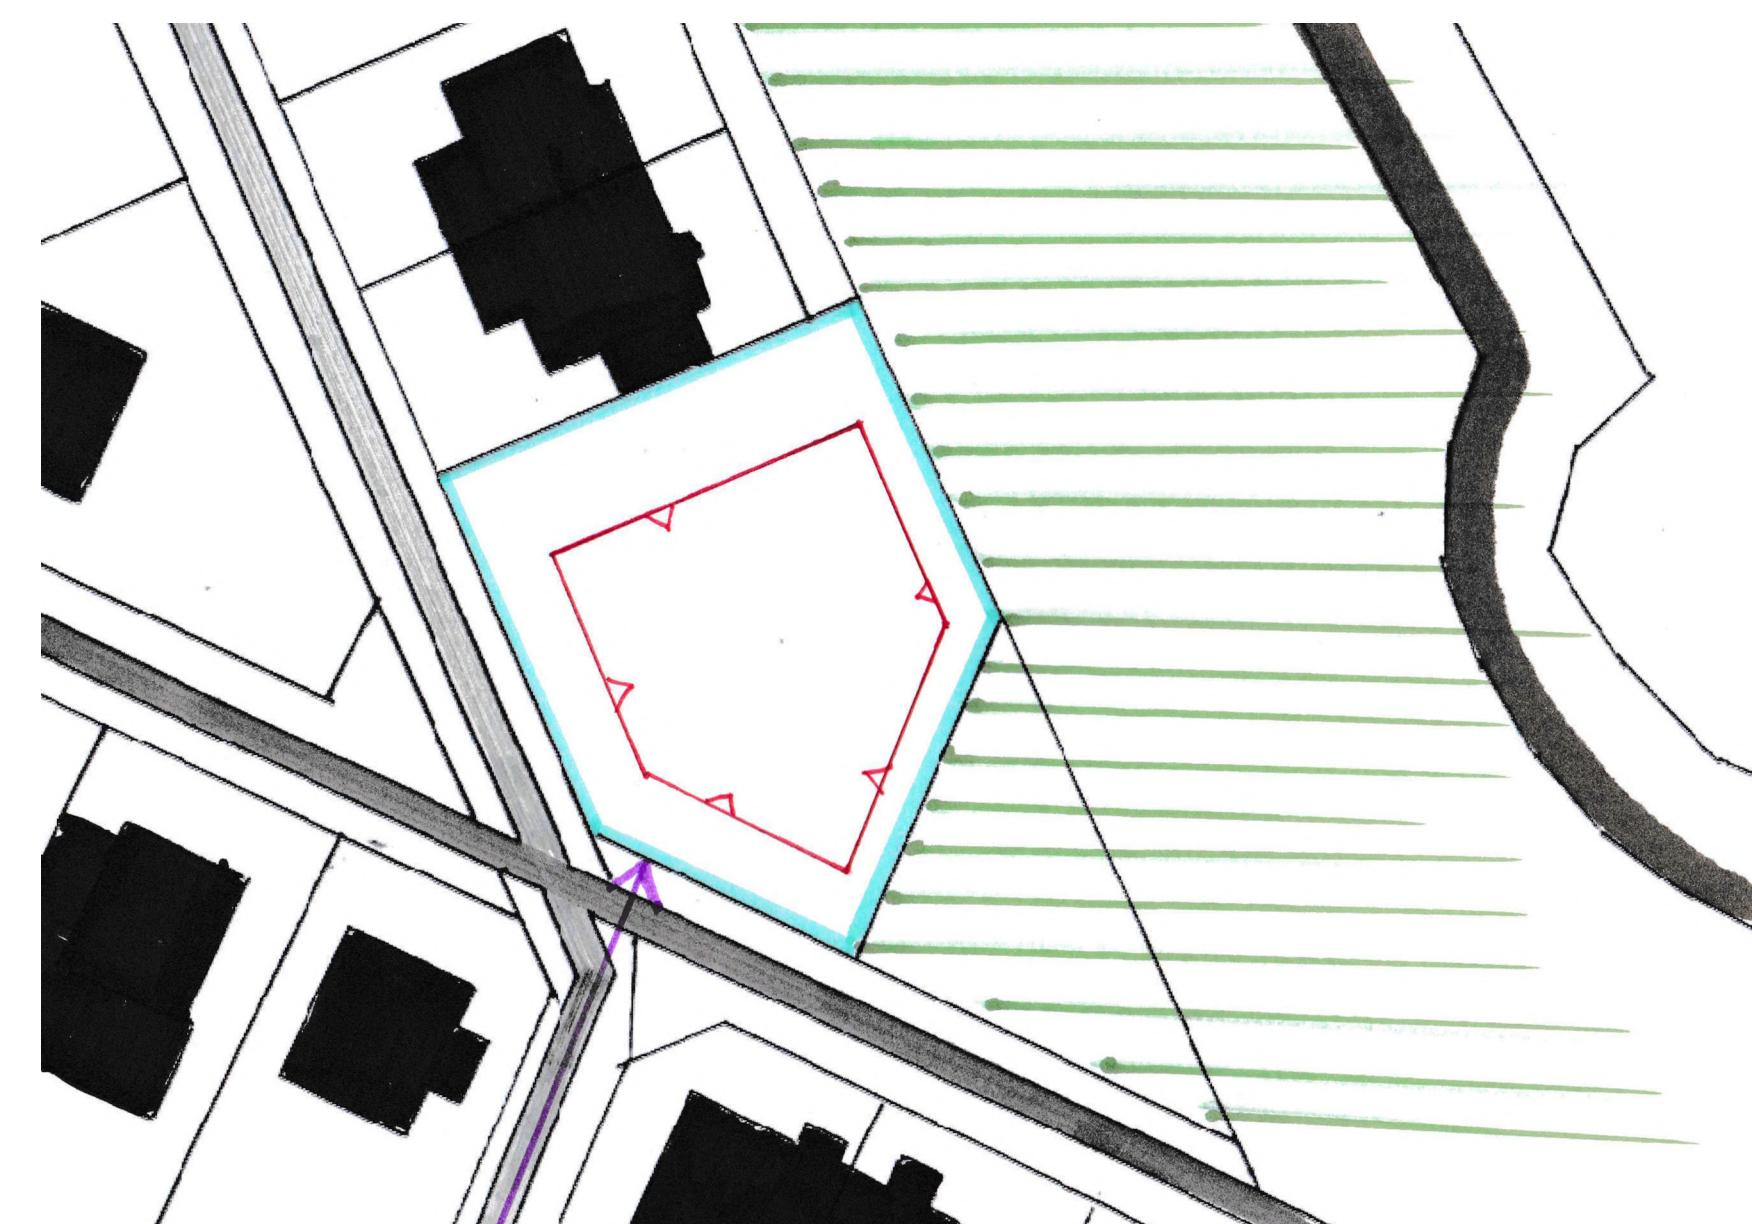

RZUT PIĘTRA SKALA 1:100

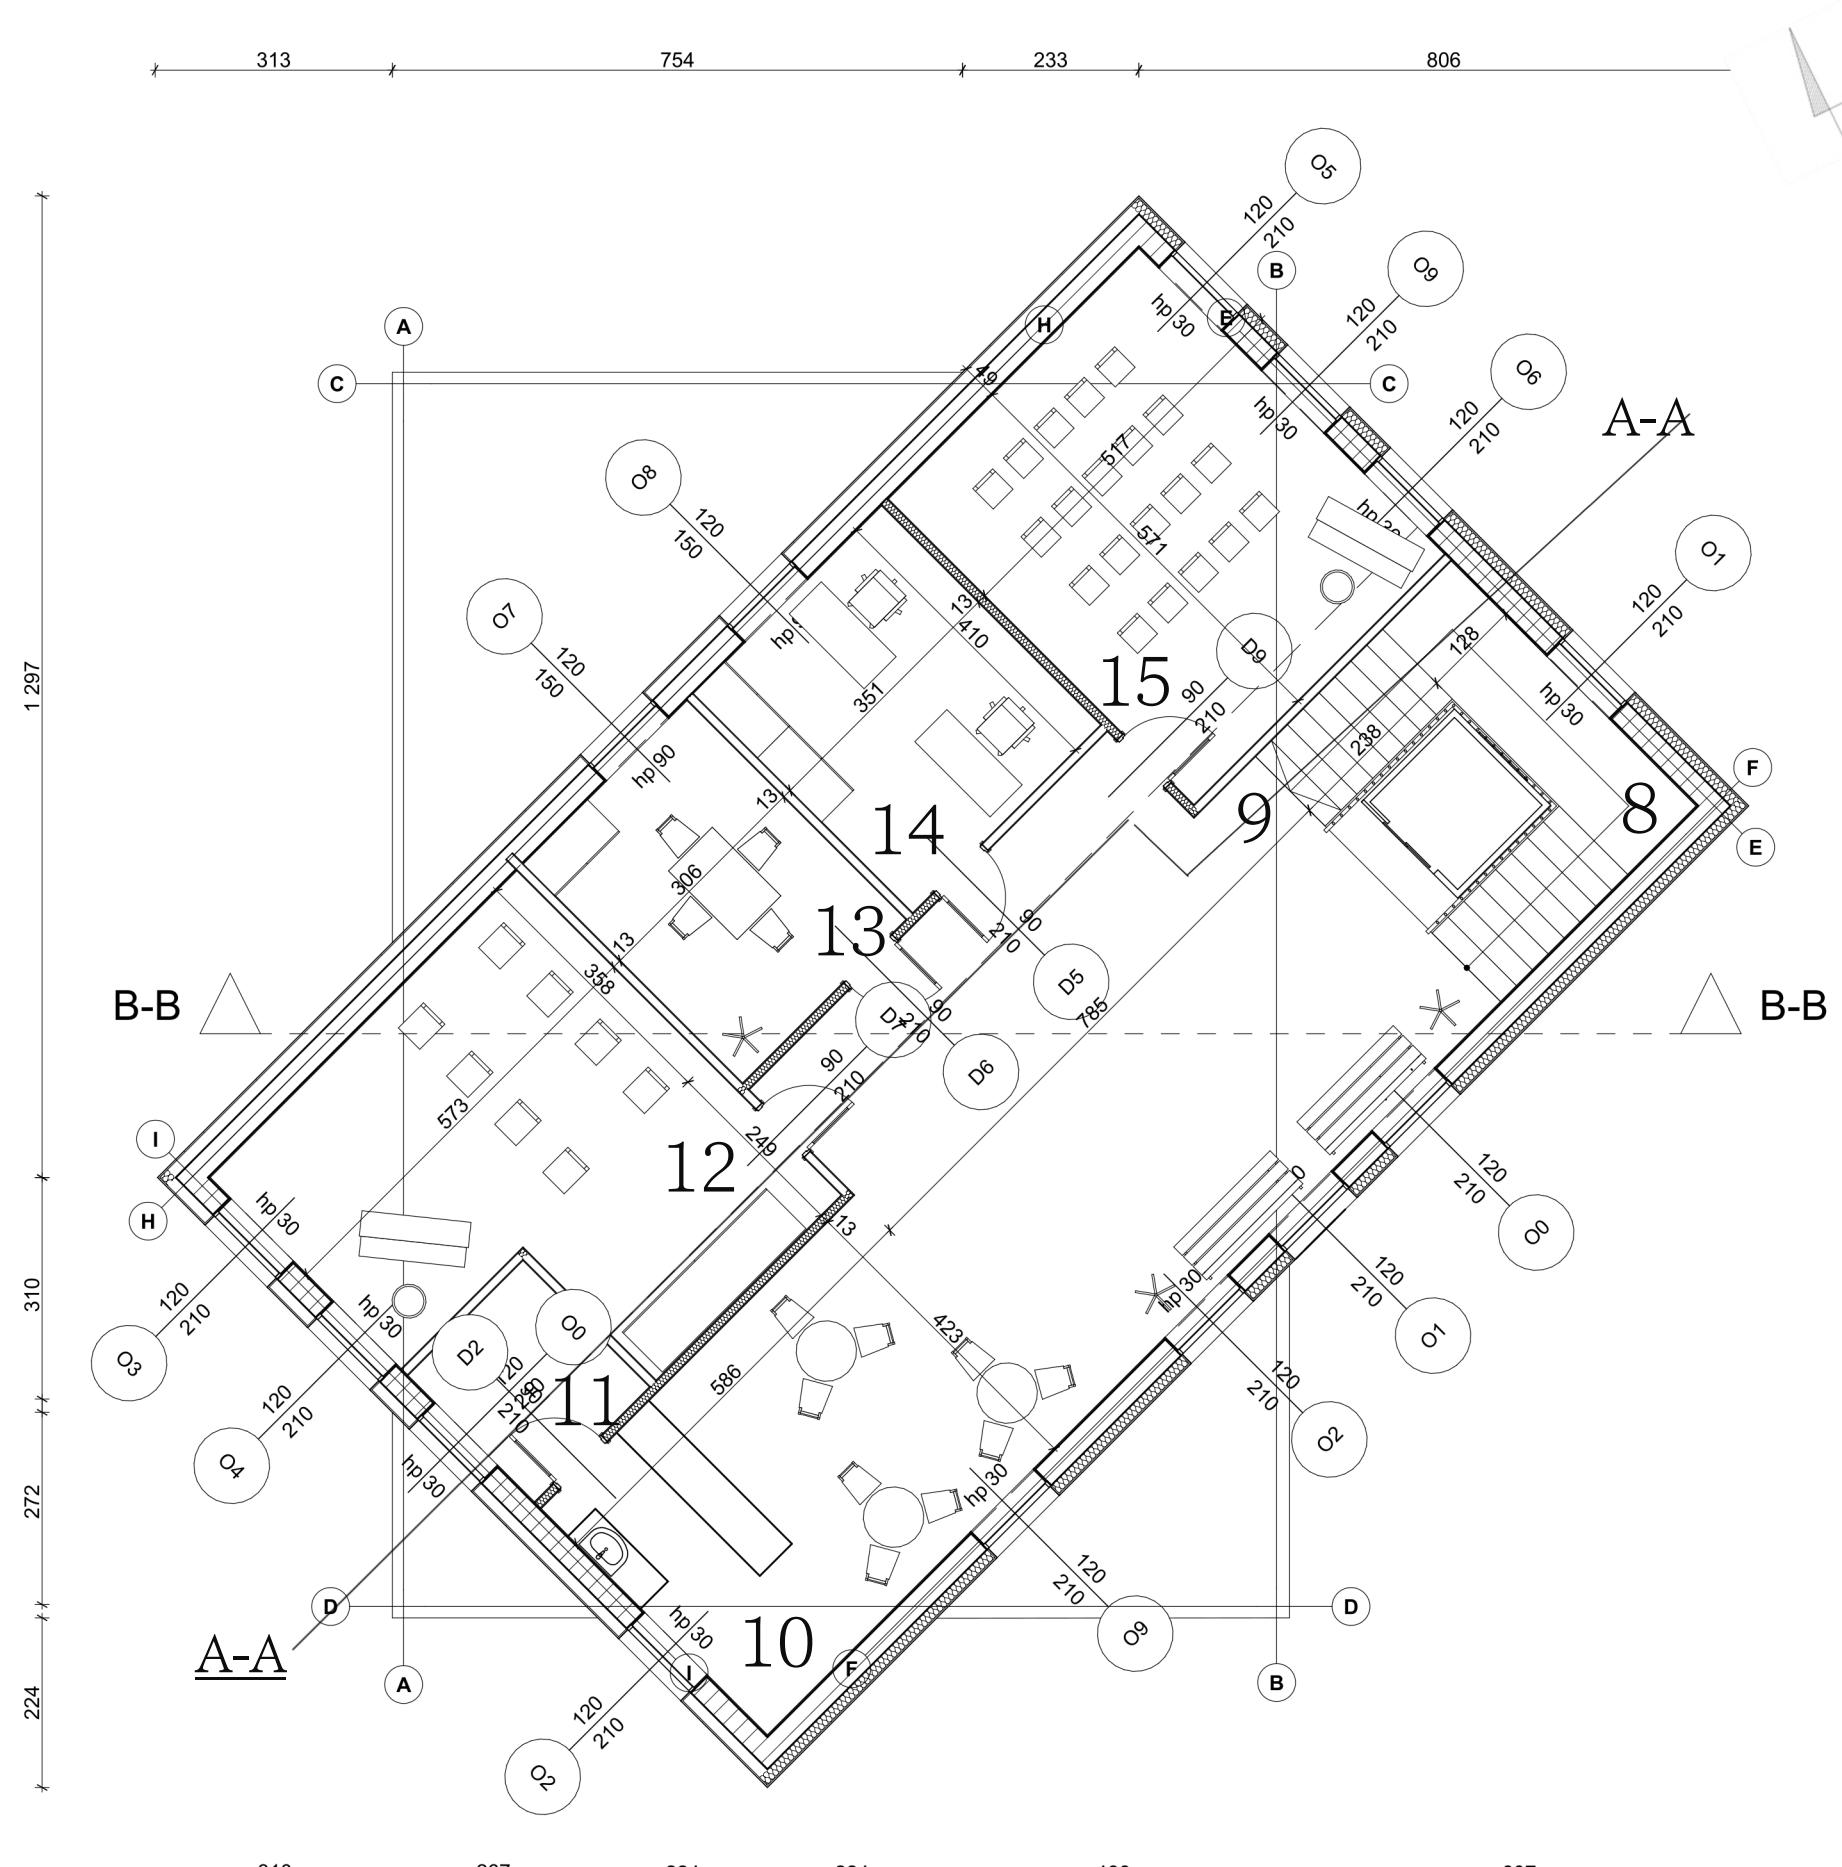


PROJEKT ZAGOSPODARIOWANIA TERENU SKALA 1:500

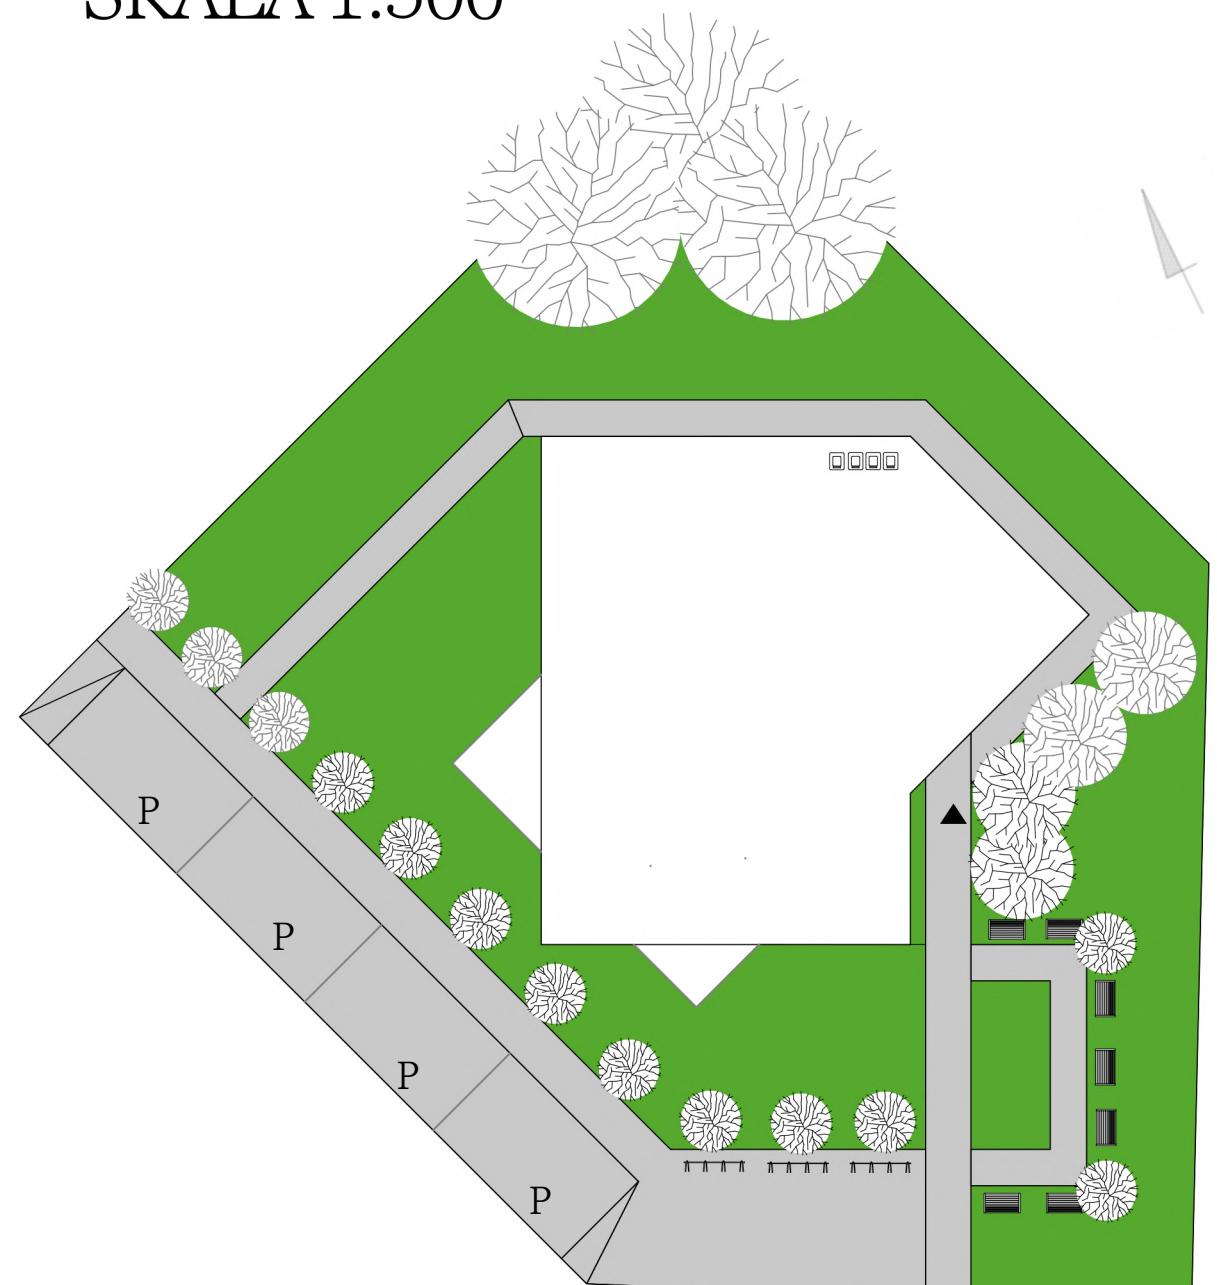

- PROJEKTOWANY BUDYNEK
- ▲ WEJŚCIE
- OGROD
- ▢ ZIELEŃ PROJEKTOWANA
- ▨ POWIERZCHNIA UTWARDZONA
- ▢ P MIEJSCA PARKINGOWE
- ▢ S ŚMIETNIK


BILANS POWIERZCHNI:
POW. ZABUDOWY
275,30 M² - 24,7 %
POW. BIOLOGICZNIE CZYNNA
514,94 M² - 49,5 %
POW. UTWARDZONA
269,06 - 25,8 %

DETAL ARCHITEKTONICZNY POSADZKA NA GRUNCIE

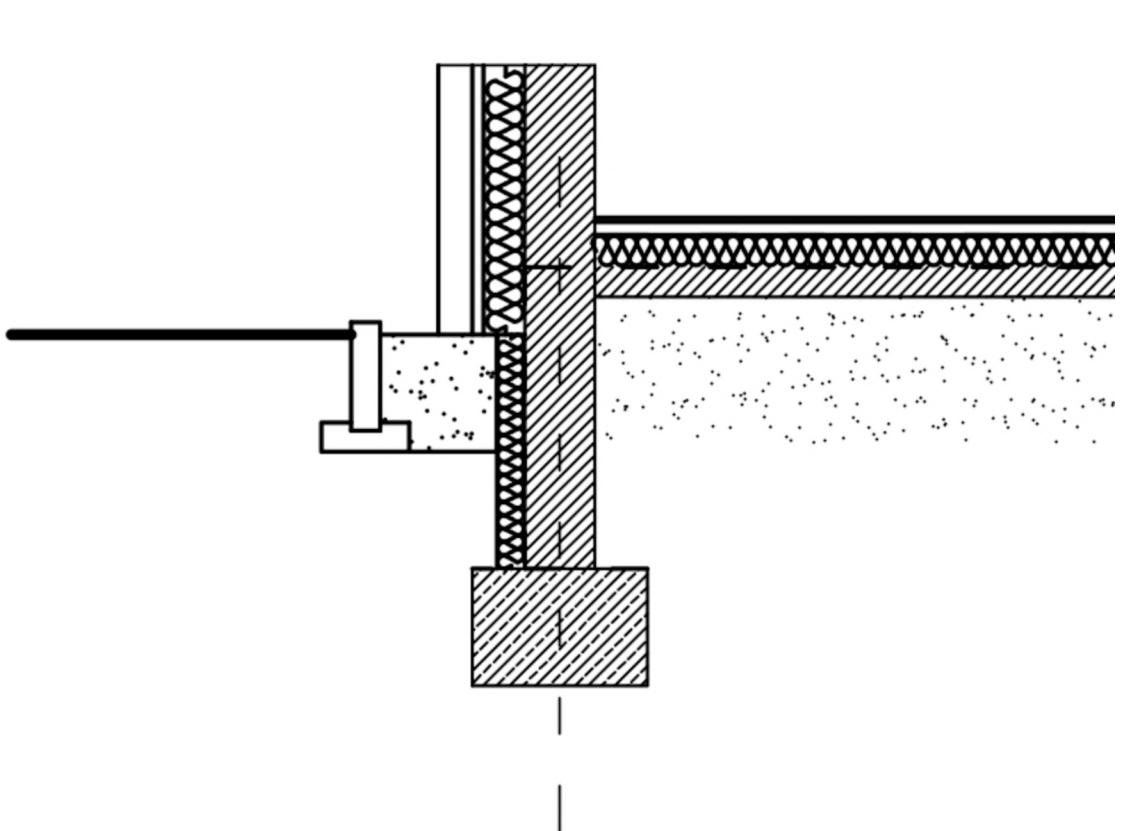


Parkiet 1,4 cm
Wylewnka betonowa 4,5 cm
Folia izolacyjna 0,2 cm
Termoizolacja - styropian 11 cm
Folia izolacyjna 0,2 cm
Posadzka betonowa 10 cm
Podsypka piaskowa 50 cm

PRZEKRÓJ A-A SKALA 1:100

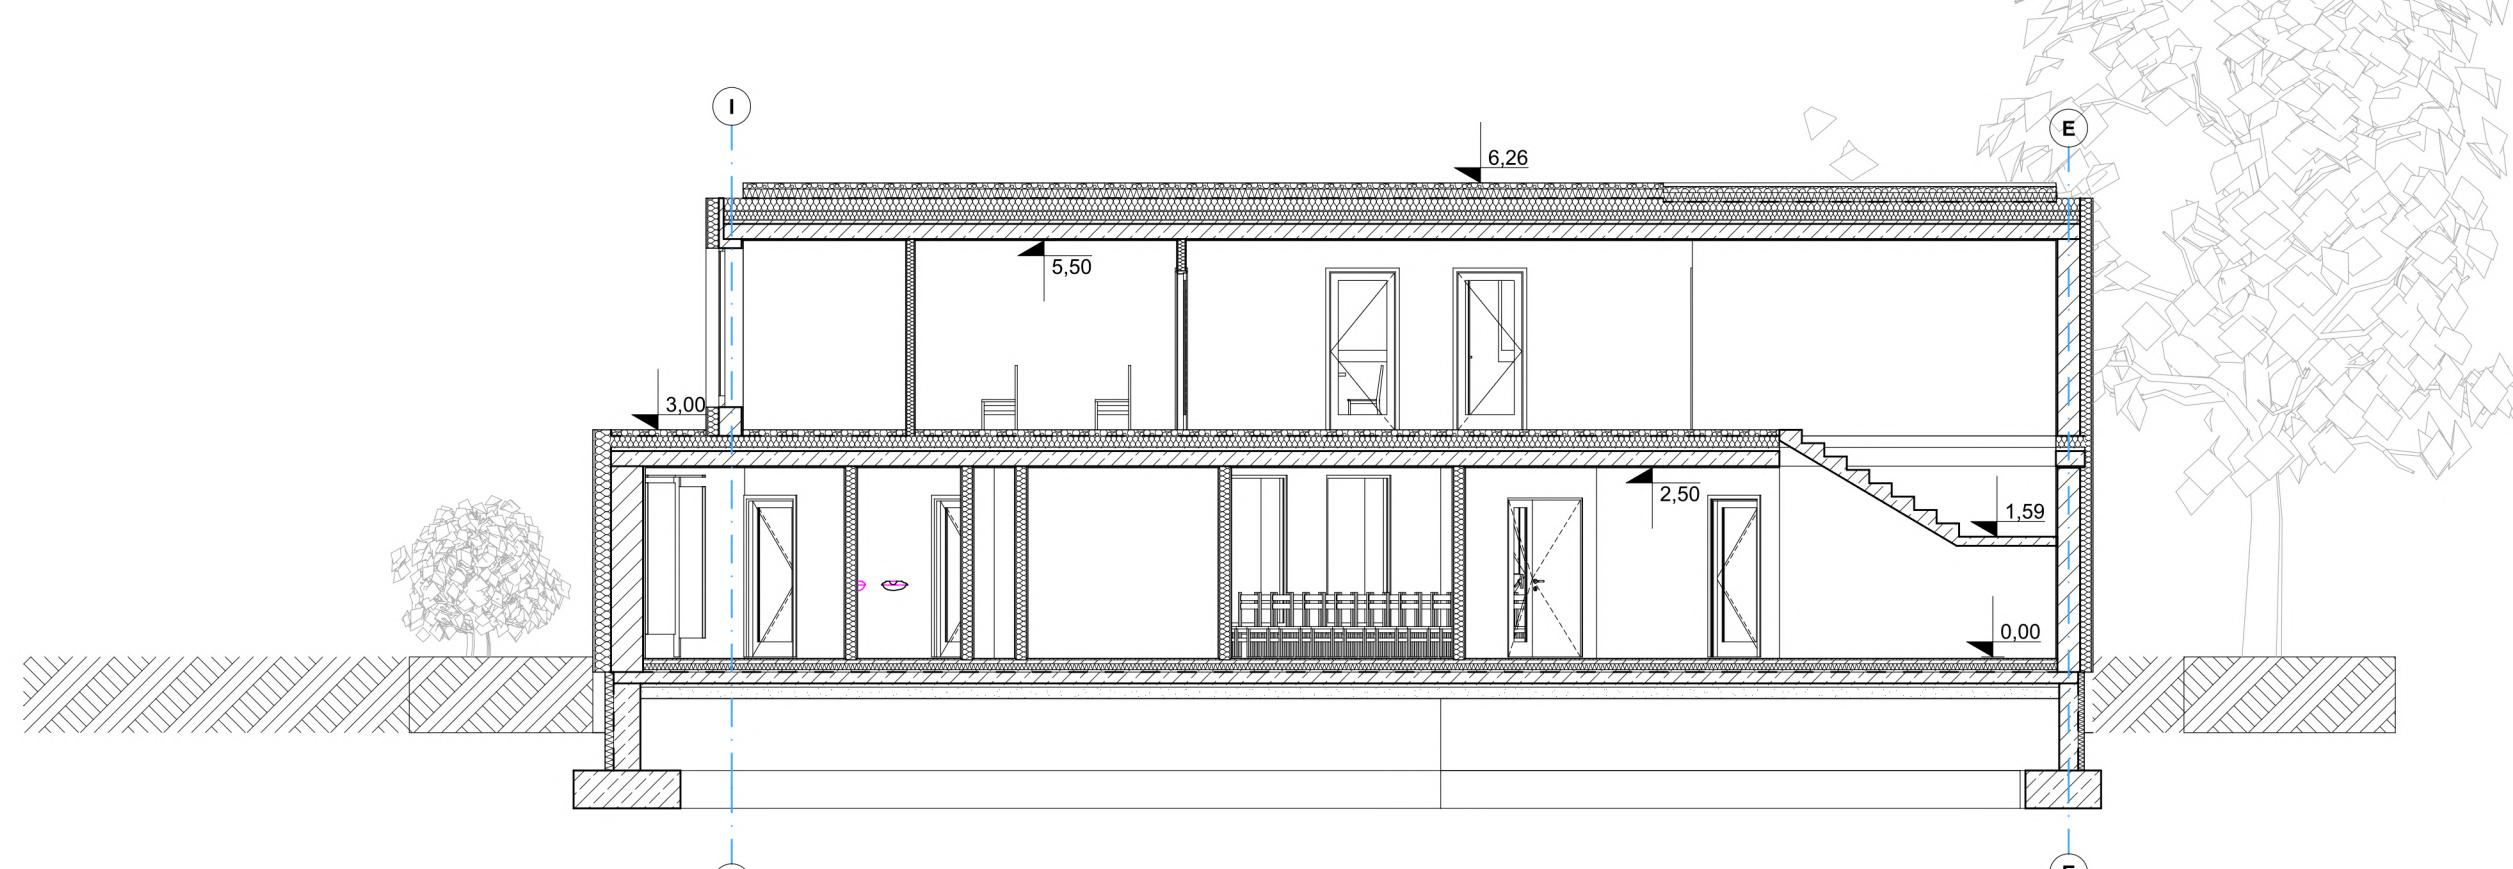

PRZEKRÓJ B-B SKALA 1:100

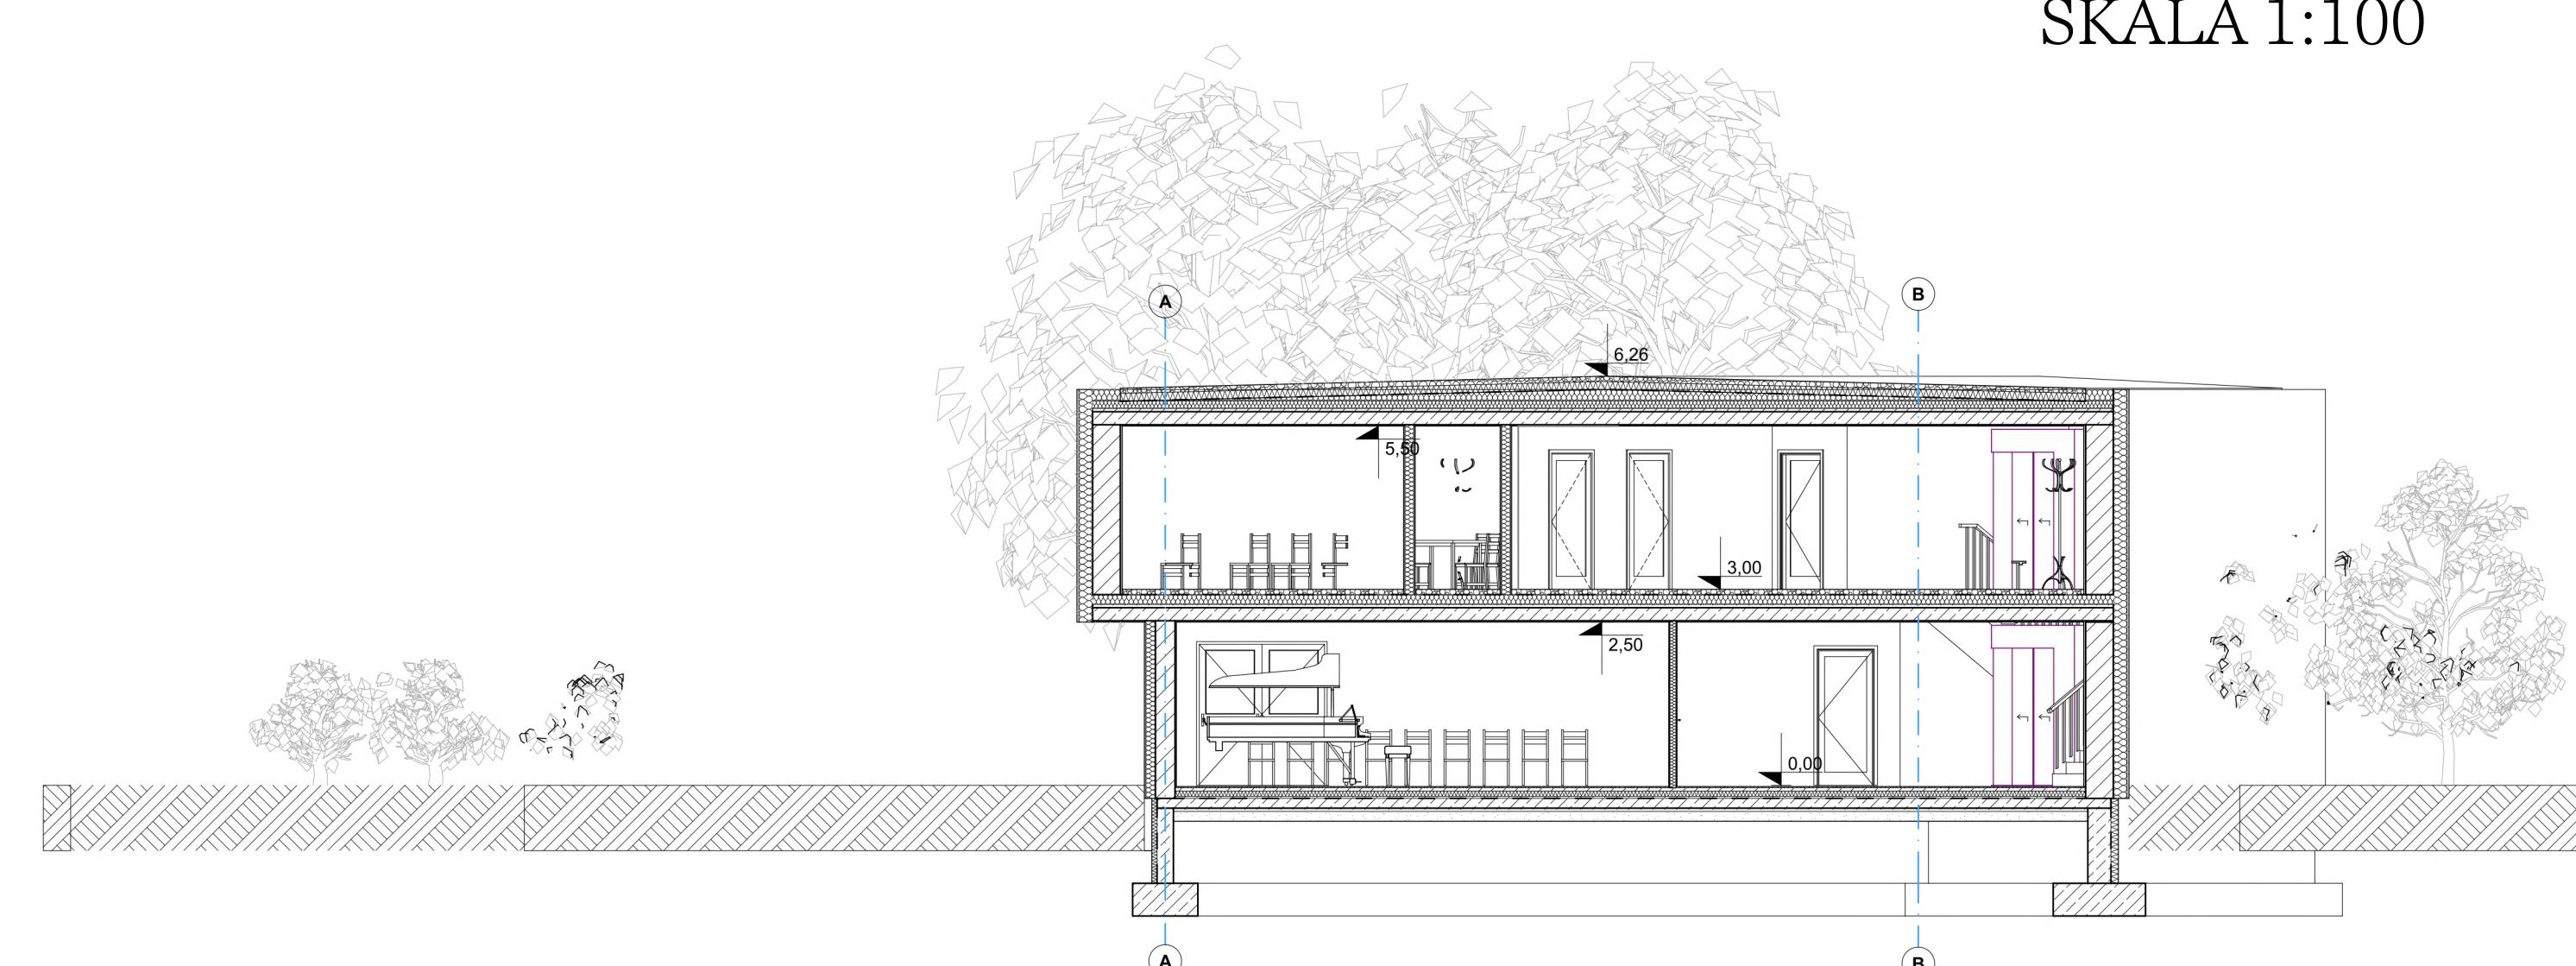

PROJEKT DOMU KULTURY PRZY ULIICY SZUBIŃSKIEJ POZNAŃ

